

SUPPLY SCOPE: Nudura 8in Standard ICF forms and accessories with the BuildEase pre-cut service, as the Distributor BOM (distributor sets its own rates). Haulage to Bosnia and Herzegovina by BuildEase Logistics quote (TBC). Alignment not included. ICF starts on the slab (slab, footings, floors, roof, partitions, windows and finishes by others - external finish and window tape quantities are a take-off only). Local building regulations and structural design by the client's engineer.

QUOTATION - NOT FOR CONSTRUCTION

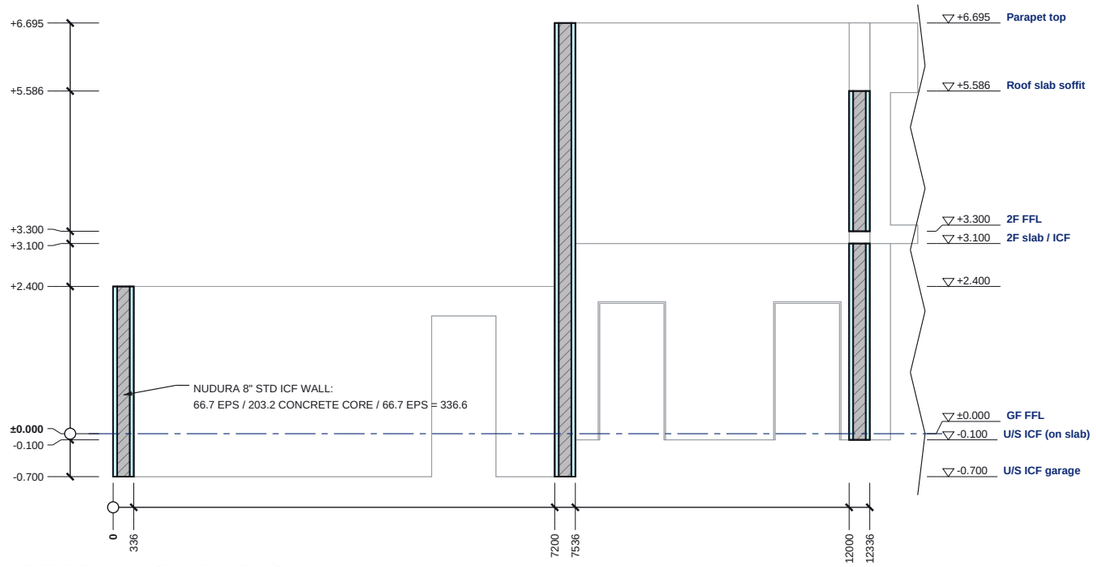

SECTION A-A (PART 1 OF 2)

Scale 1:100 @ A3 | Looking west; levels above GF FFL

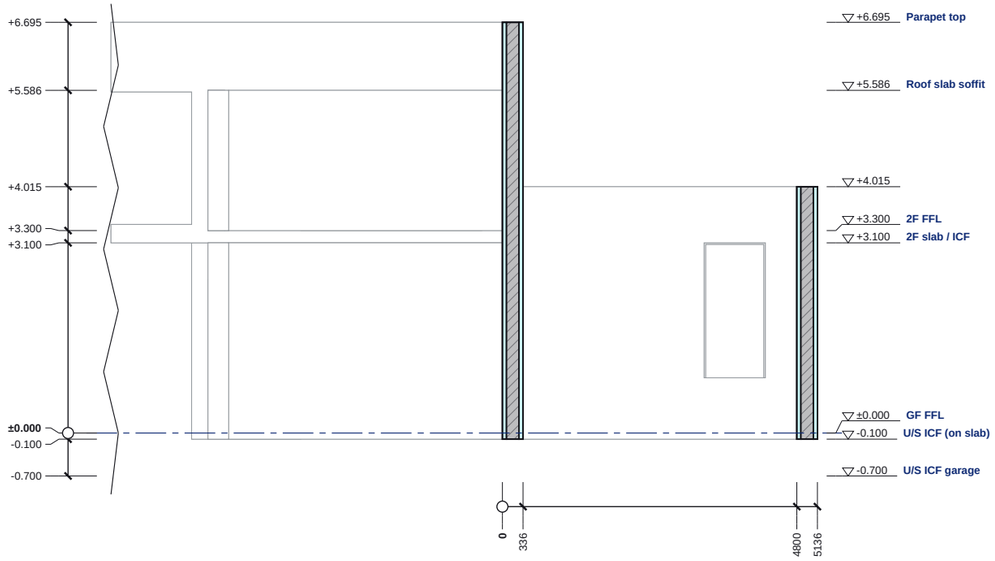

SECTION A-A (PART 2 OF 2)

Scale 1:100 @ A3 | Looking west; levels above GF FFL

ICF EPS (cut)
ICF concrete core / RC (cut)
Steel (cut)
Beyond the cut (line work)


0 1 2 3 4 5m

SECTION A-A SCHEDULES

LEVELS ON THIS SECTION

Level	FFL
U/S ICF garage	-0.700
U/S ICF (on slab)	-0.100
GF FFL	±0.000
top of ICF W13	+2.400
2F slab / ICF	+3.100
2F FFL	+3.300
top of ICF W02	+4.015
Roof slab soffit	+5.586
Parapet top	+6.695

SECTION KEY

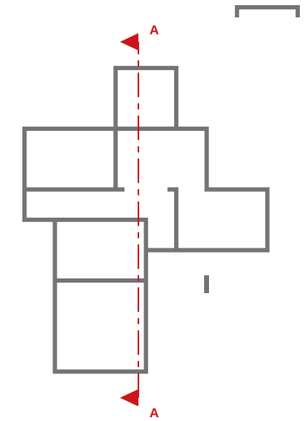

NOTES

1. Section A-A is a BuildEase ICF section (not an architect's section line). Cut elements hatched / filled; the model beyond the cut in line work.
2. Levels above GF FFL.
3. ICF: Nudura 8" Std, 66.7 EPS + 203.2 core + 66.7 EPS = 336.6, 203.2 core + 66.7 EPS = 336.6. No structural design (architect's project drawings). ICF per the quotation model: Nudura 8in Standard external walls and the 200 monolithic internal load-bearing walls; masonry partitions excluded. Floors, roof slab, lintels and reinforcement by the engineer.
4. Steel marks, BOS / TOS: rev -. See ES26-086-GA-01 / EL-01 / EL-02 in the approval drawings pack.

REVISIONS

REV	DATE	DESCRIPTION
-	02.11.26	Quotation issue

Nudura™ BuildEase

CLIENT	PROJECT
Tremco CPG Poland	Villa Bosnia - Nudura model house, Bosnia and Herzegovina

DRAWING TITLE
SECTION A-A
ICF section with levels and build-ups

SCALE	SIZE	DATE
1:100	A3	02.11.26
DRAWN	CHECKED	APPROVED
TS		

STATUS	DRAWING No.	REV
QUOTATION	ES26-086-SE-01	-

Do not scale. All dimensions in millimetres, levels in metres from GF FFL. Check all dimensions on site.