
SUPPLY SCOPE: Nudura 8in Standard ICF forms and accessories with the BuildEase pre-cut service, as the Distributor BOM (distributor sets its own rates). Haulage to Bosnia and Herzegovina by BuildEase Logistics quote (TBC). Alignment not included. ICF starts on the slab. Slabs, roof, stair, partitions, windows and doors are drawn in good faith for coordination only (by others / engineer); finishes by others - external finish and window tape quantities are a take-off only). Local building regulations and structural design by the client's engineer.

QUOTATION - NOT FOR CONSTRUCTION

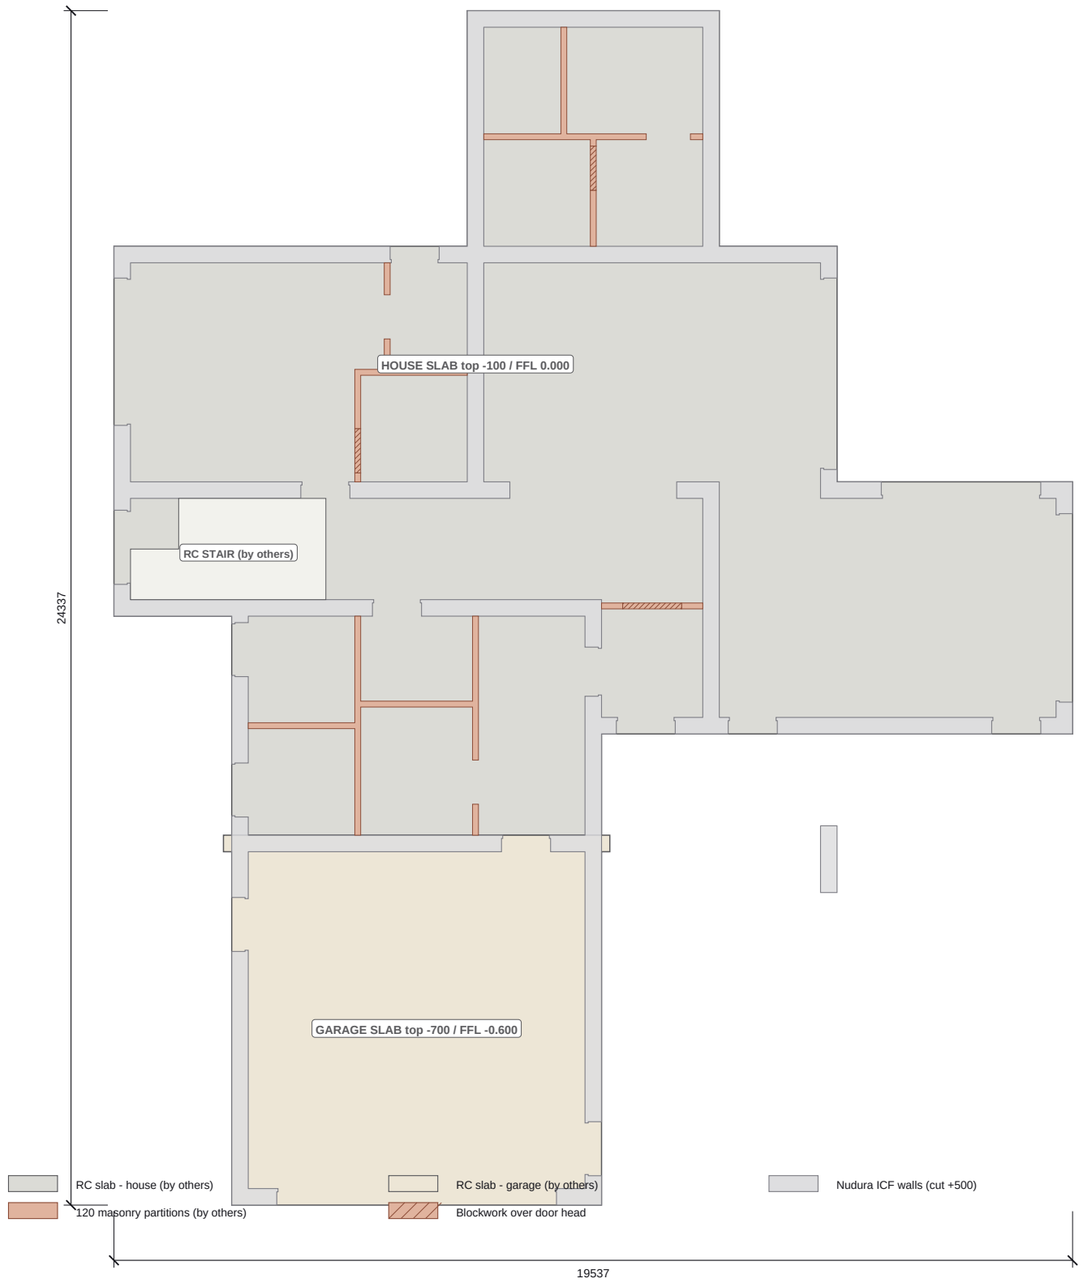

GROUND SLAB PLAN

Scale 1:125 @ A3 | RC slab by others; ICF walls cut at +500

0 1 2 3 4 5m

GROUND SLAB SCHEDULES

BUILD-UP

Zone / layer	mm	Top
House - RC slab	250	-100
House - insulation + screed	100	0 (FFL)
Garage - RC slab	250	-700
Garage - screed	100	-600

AREAS

Item	m2
RC slab - house	205.6
RC slab - garage	56.9
Insulation + screed - house	173.2
Screed - garage	47.1
RC slab total (m3 @ 250)	**65.6**

Plan areas from the model outline; indicative, by others.

NOTES

1. RC ground-bearing slab / raft BY OTHERS (engineer): 250 thick, top -0.100 under the ICF in the house and -0.700 in the garage (section 1-1). The ICF starts on the slab - no footing blocks. Starter bars, DPM, sub-base and any thickenings under the walls to the engineer.
2. Floor build-up (by others): house 100 rigid insulation + screed to the GF FFL 0.000; garage 100 screed to -0.600. Drawn for pricing / coordination only.
3. Masonry partitions (120 blockwork, by others) shown brick-red, 13 pieces, cut to the ICF inner face; hatched = blockwork over a door head (+2.100). Partitions sit on the slab, not on the screed.
4. Levels relative to the GF FFL 0.000, mm.

REVISIONS

REV	DATE	DESCRIPTION
-	02.11.26	Quotation issue

Nudura™ BuildEase

CLIENT	PROJECT
Tremco CPG Poland	Villa Bosnia - Nudura model house, Bosnia and Herzegovina

DRAWING TITLE

GROUND SLAB

RC ground slab, floor build-ups, GF partitions

SCALE	SIZE	DATE
1:125	A3	02.11.26
DRAWN	**CHECKED**	**APPROVED**
TS		

STATUS	DRAWING No.	REV
QUOTATION	ES26-086-FL-01	-

Do not scale. All dimensions in mm. Check all dimensions on site.