
SUPPLY SCOPE: Nudura 8in Standard ICF forms and accessories with the BuildEase pre-cut service, as the Distributor BOM (distributor sets its own rates). Haulage to Bosnia and Herzegovina by BuildEase Logistics quote (TBC). Alignment not included. ICF starts on the slab. Slabs, roof, stair, partitions, windows and doors are drawn in good faith for coordination only (by others / engineer); finishes by others - external finish and window tape quantities are a take-off only). Local building regulations and structural design by the client's engineer.

QUOTATION - NOT FOR CONSTRUCTION

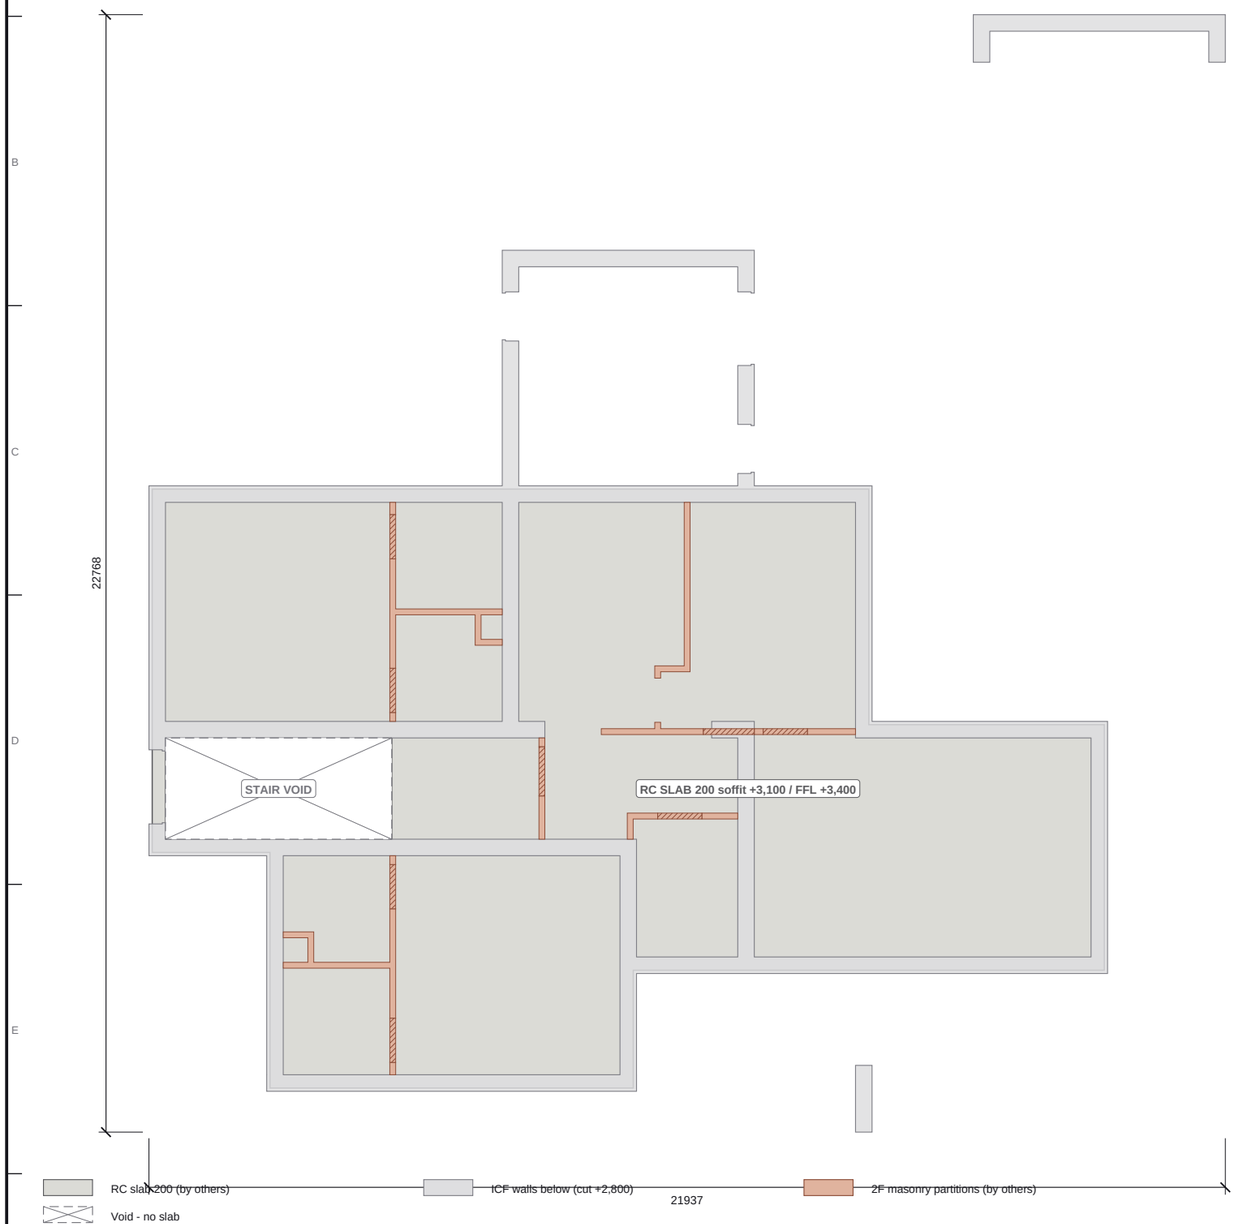

SECOND FLOOR SLAB PLAN

Scale 1:125 @ A3 | RC slab by others; ICF walls below cut at +2,800

0 1 2 3 4 5m

Do not scale. All dimensions in mm. Check all dimensions on site.

SECOND FLOOR SLAB SCHEDULES

BUILD-UP

Layer	mm	Top
FFL	-	+3,400
Insulation + screed	100	+3,400
RC slab	200	+3,300
Soffit	-	+3,100

AREAS

Item	m2
RC slab (net of void)	169.7
Stair void	9.5
Insulation + screed	143.7
RC slab (m3 @ 200)	**33.9**

NOTES

1. RC suspended slab BY OTHERS (engineer): 200 thick, soffit +3.100, top +3.300, bearing on the concrete core of the Nudura walls below (ICF inner panel cut back at the slab line / ledger detail to the engineer).
2. 100 insulation + screed to the 2F FFL +3.400 (section 1-1). Stair void trimmed in the slab - edge reinforcement to the engineer.
3. 2F masonry partitions (120 blockwork, by others) brick-red, 22 pieces; hatched = over a door head (+5.600).
4. Drawn for pricing / coordination only. Levels relative to the GF FFL 0.000, mm.

REVISIONS

REV	DATE	DESCRIPTION
-	02.11.26	Quotation issue

Nudura™ BuildEase

CLIENT	PROJECT
Tremco CPG Poland	Villa Bosnia - Nudura model house, Bosnia and Herzegovina

DRAWING TITLE

SECOND FLOOR SLAB

RC 2F slab, stair void, 2F partitions

SCALE	SIZE	DATE
1:125	A3	02.11.26
DRAWN	CHECKED	APPROVED
TS		

STATUS	DRAWING No.	REV
QUOTATION	ES26-086-FL-02	-