
SUPPLY SCOPE: Nudura 8in Standard ICF forms and accessories with the BuildEase pre-cut service, as the Distributor BOM (distributor sets its own rates). Haulage to Bosnia and Herzegovina by BuildEase Logistics quote (TBC). Alignment not included. ICF starts on the slab. Slabs, roof, stair, partitions, windows and doors are drawn in good faith for coordination only (by others / engineer); finishes by others - external finish and window tape quantities are a take-off only). Local building regulations and structural design by the client's engineer.

QUOTATION - NOT FOR CONSTRUCTION

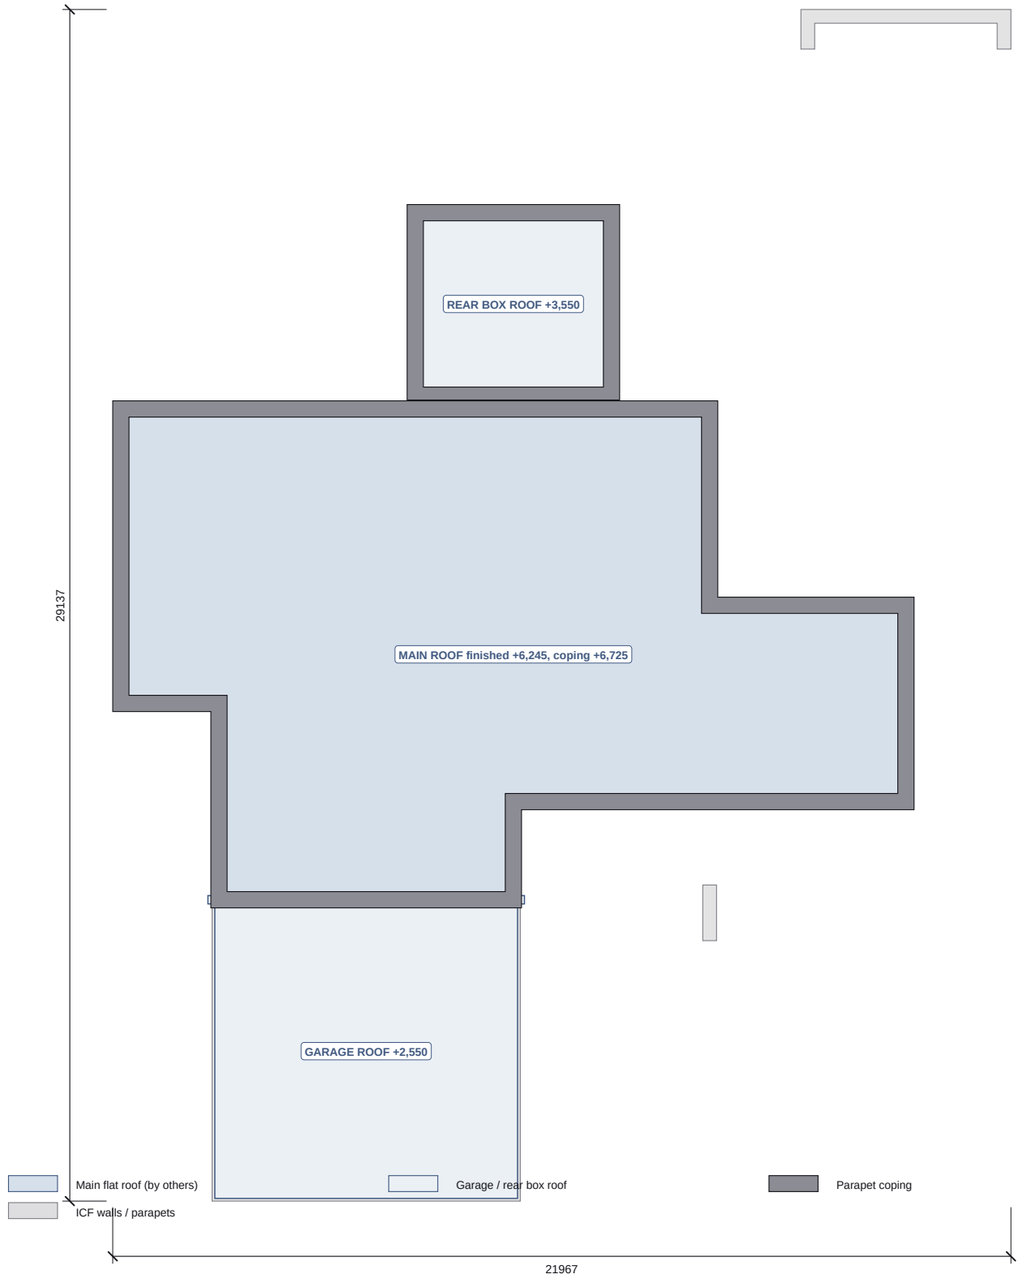

ROOF PLAN

Scale 1:150 @ A3 | Roofs by others; ICF parapets cut at +6,400 (main) and +2,100 (garage / rear box)

0 1 2 3 4 5m

ROOF SCHEDULES

MAIN ROOF BUILD-UP

Layer	mm	Top
Coping (parapet)	30	+6,725
Waterproofing + ballast	200	+6,245
Insulation to falls + screed	260	+6,045
RC roof slab	200	+5,785
Soffit	-	+5,585

AREAS

Roof	m2
Main roof slab	179.2
Main roof waterproofing (inside parapet)	162.4
Garage roof	54.9
Rear box roof	23.4
Coping run, main + rear box (m)	80.8

Coping run = mean of the coping ring perimeters.

NOTES

1. MAIN FLAT ROOF (by others / engineer): RC slab 200 soffit +5.585, insulation to falls + screed to +6.045, waterproofing + ballast to +6.245 inside the ICF parapet; parapet coping +6.695 to +6.725 (section 1-1). Falls, outlets and overflows to the roofing designer.
2. GARAGE ROOF: RC slab 200 +2.200 to +2.400 on the garage walls, insulation + waterproofing to +2.550. REAR BOX ROOF: RC slab 200 +3.100 to +3.300, build-up to +3.550, ICF parapet to the coping +4.015 to +4.045.
3. Parapet heights and roof build-ups assumed from section 1-1 - RFI. Upstands >= 150 above the finished roof.
4. Drawn for pricing / coordination only. Levels relative to the GF FFL 0.000, mm.

REVISIONS

REV	DATE	DESCRIPTION
-	02.11.26	Quotation issue

Nudura™ BuildEase

CLIENT	PROJECT
Tremco CPG Poland	Villa Bosnia - Nudura model house, Bosnia and Herzegovina

DRAWING TITLE

ROOF PLAN

Main flat roof, garage roof, rear box roof

SCALE	SIZE	DATE
1:150	A3	02.11.26
DRAWN	CHECKED	APPROVED
TS		

STATUS	DRAWING No.	REV
QUOTATION	ES26-086-RF-01	-

Do not scale. All dimensions in mm. Check all dimensions on site.