
SUPPLY SCOPE: Nudura 8in Standard ICF forms and accessories with the BuildEase pre-cut service, as the Distributor BOM (distributor sets its own rates). Haulage to Bosnia and Herzegovina by BuildEase Logistics quote (TBC). Alignment not included. ICF starts on the slab. Slabs, roof, stair, partitions, windows and doors are drawn in good faith for coordination only (by others / engineer); finishes by others - external finish and window tape quantities are a take-off only). Local building regulations and structural design by the client's engineer.

QUOTATION - NOT FOR CONSTRUCTION

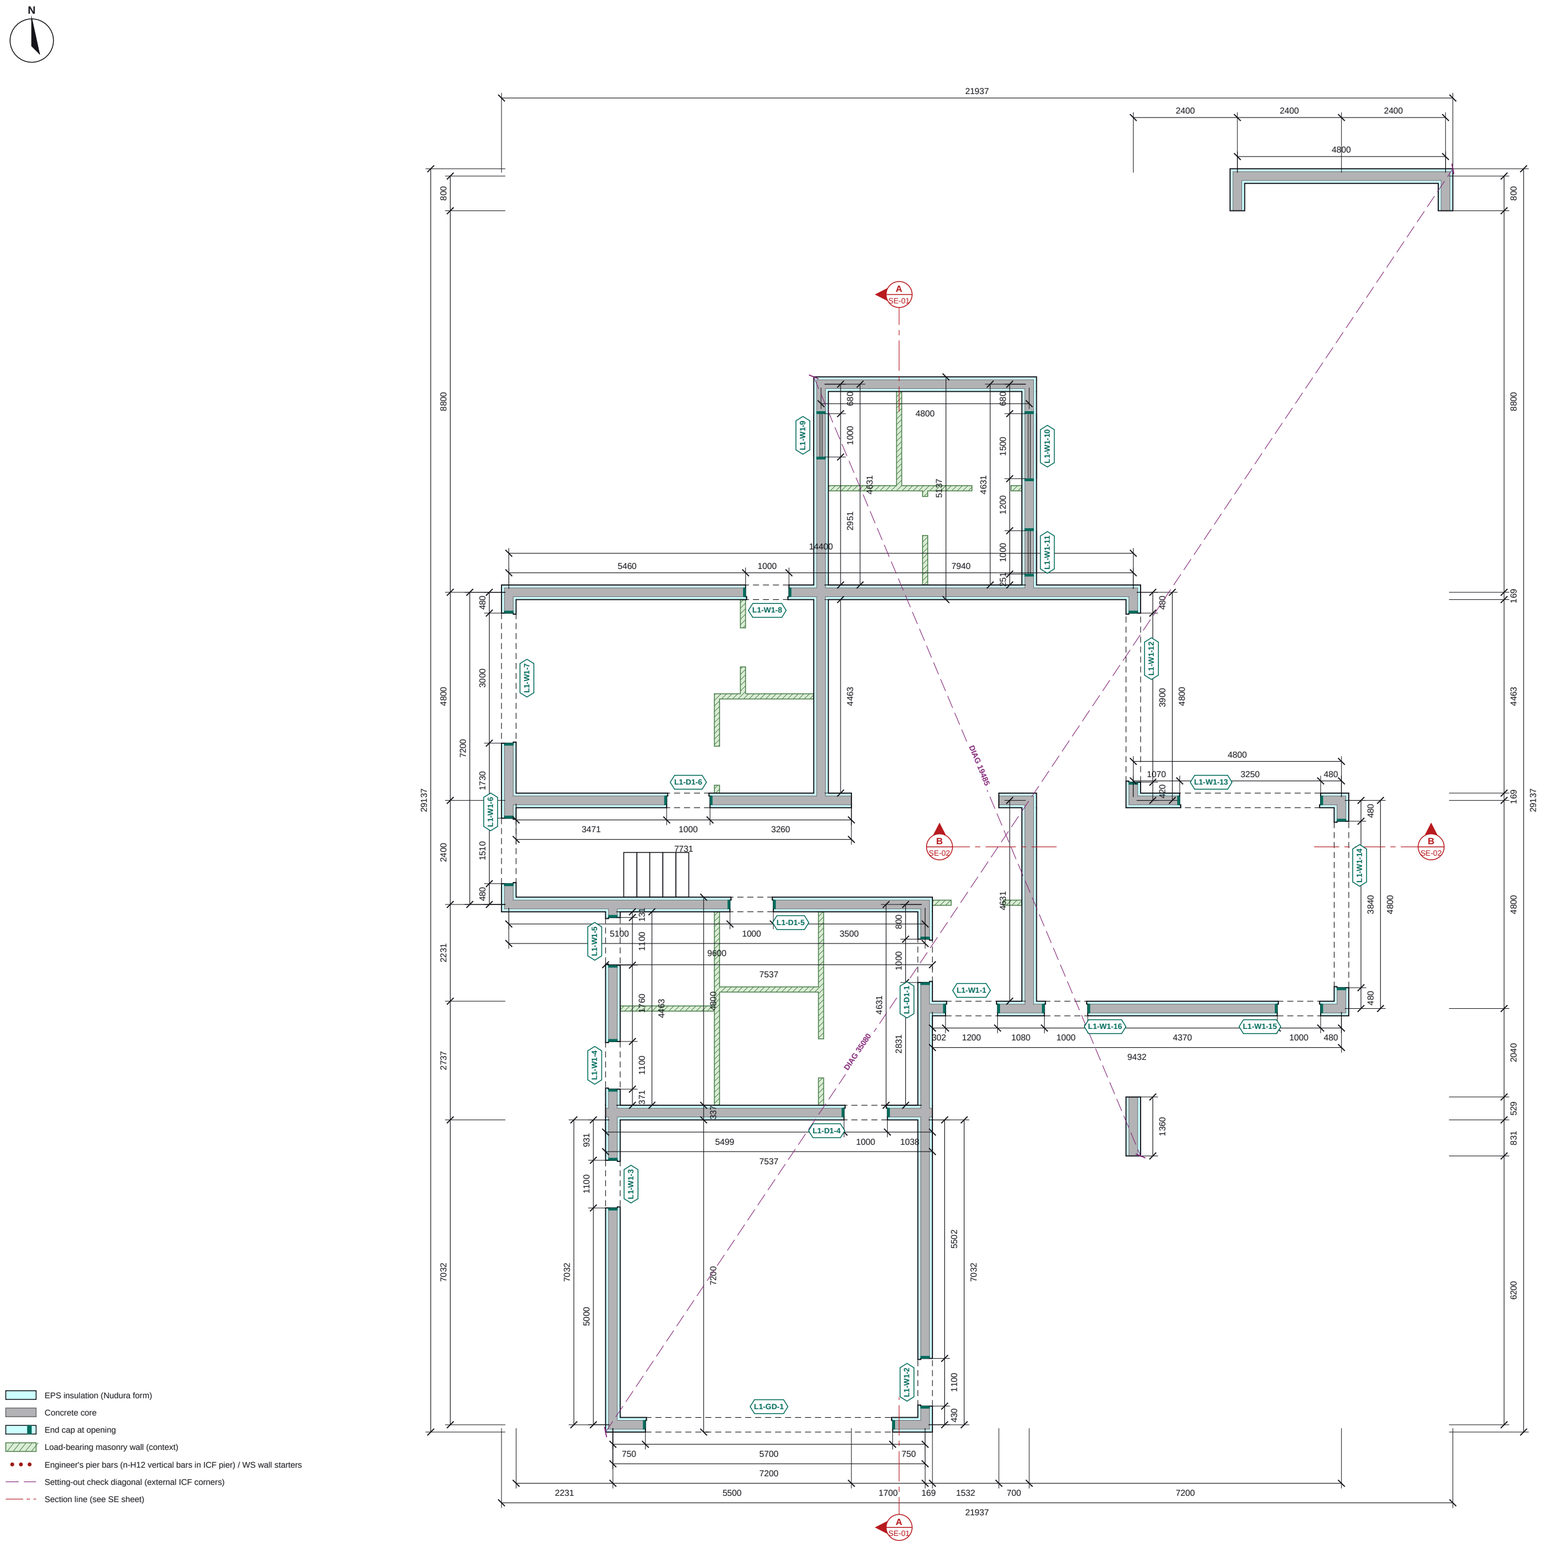

- EPS insulation (Nudura form)
- Concrete core
- End cap at opening
- Load-bearing masonry wall (context)
- Engineer's pier bars (n-H12 vertical bars in ICF pier) / WS wall starters
- Setting-out check diagonal (external ICF corners)
- Section line (see SE sheet)

GROUND FLOOR ICF PLAN

Scale 1:100 @ A2 | Plan cut at +780

0 1 2 3 4 5m

GROUND FLOOR ICF SCHEDULES

OPENING SCHEDULE

Ref	Width	Height	Sill	Head	Lintel
L1-W1-3	1100	2645	-700	+1945	-
L1-GD-1	5700	2645	-700	+1945	-
L1-W1-2	1100	2645	-700	+1945	-
L1-W1-5	1100	2250	-100	+2150	-
L1-W1-4	1100	2250	-100	+2150	-
L1-W1-6	1510	3200	-100	+3100	-
L1-W1-7	3000	2743	-100	+2643	-
L1-W1-8	1000	2743	-100	+2643	-
L1-W1-11	1000	2200	+900	+3100	-
L1-W1-10	1500	2200	+900	+3100	-
L1-W1-12	3900	2743	-100	+2643	-
L1-W1-13	3250	2743	-100	+2643	-
L1-W1-14	3840	2743	-100	+2643	-
L1-W1-16	1000	2743	-100	+2643	-
L1-W1-15	1000	2743	-100	+2643	-
L1-W1-1	1200	2743	-100	+2643	-
L1-W1-9	1000	2200	+900	+3100	-
L1-D1-4	1000	2800	-700	+2100	-
L1-D1-1	1000	2600	-100	+2500	-
L1-D1-5	1000	2600	-100	+2500	-
L1-D1-6	1000	2600	-100	+2500	-

Structural openings in the ICF; sill and head above GF FFL.

NOTES

1. ICF: Nudura 8" Std, 66.7 EPS + 203.2 core + 66.7 EPS = 336.6. Dimensions to the ICF faces.
2. Levels above GF FFL. Sill / head = structural opening in the ICF.
3. No structural design (architect's project drawings). ICF per the quotation model: Nudura 8in Standard external walls and the 200 monolithic internal load-bearing walls; masonry partitions excluded. Floors, roof slab, lintels and reinforcement by the engineer.
4. Lintel (L-n) and steel (B-n, C-1) marks from rev -, which takes precedence.
5. Masonry walls shown for context.

REVISIONS

REV	DATE	DESCRIPTION
-	02.11.26	Quotation issue

Nudura™ BuildEase

CLIENT	PROJECT
Tremco CPG Poland	Villa Bosnia - Nudura model house, Bosnia and Herzegovina

DRAWING TITLE

GROUND FLOOR ICF GENERAL ARRANGEMENT

ICF walls, openings, lintels, steel over and engineer's notes

SCALE	SIZE	DATE
1:100	A2	02.11.26
DRAWN	CHECKED	APPROVED
TS		

STATUS	DRAWING No.	REV
QUOTATION	ES26-086-GA-01	-

Do not scale. All dimensions in millimetres, levels in metres from GF FFL. Check all dimensions on site.